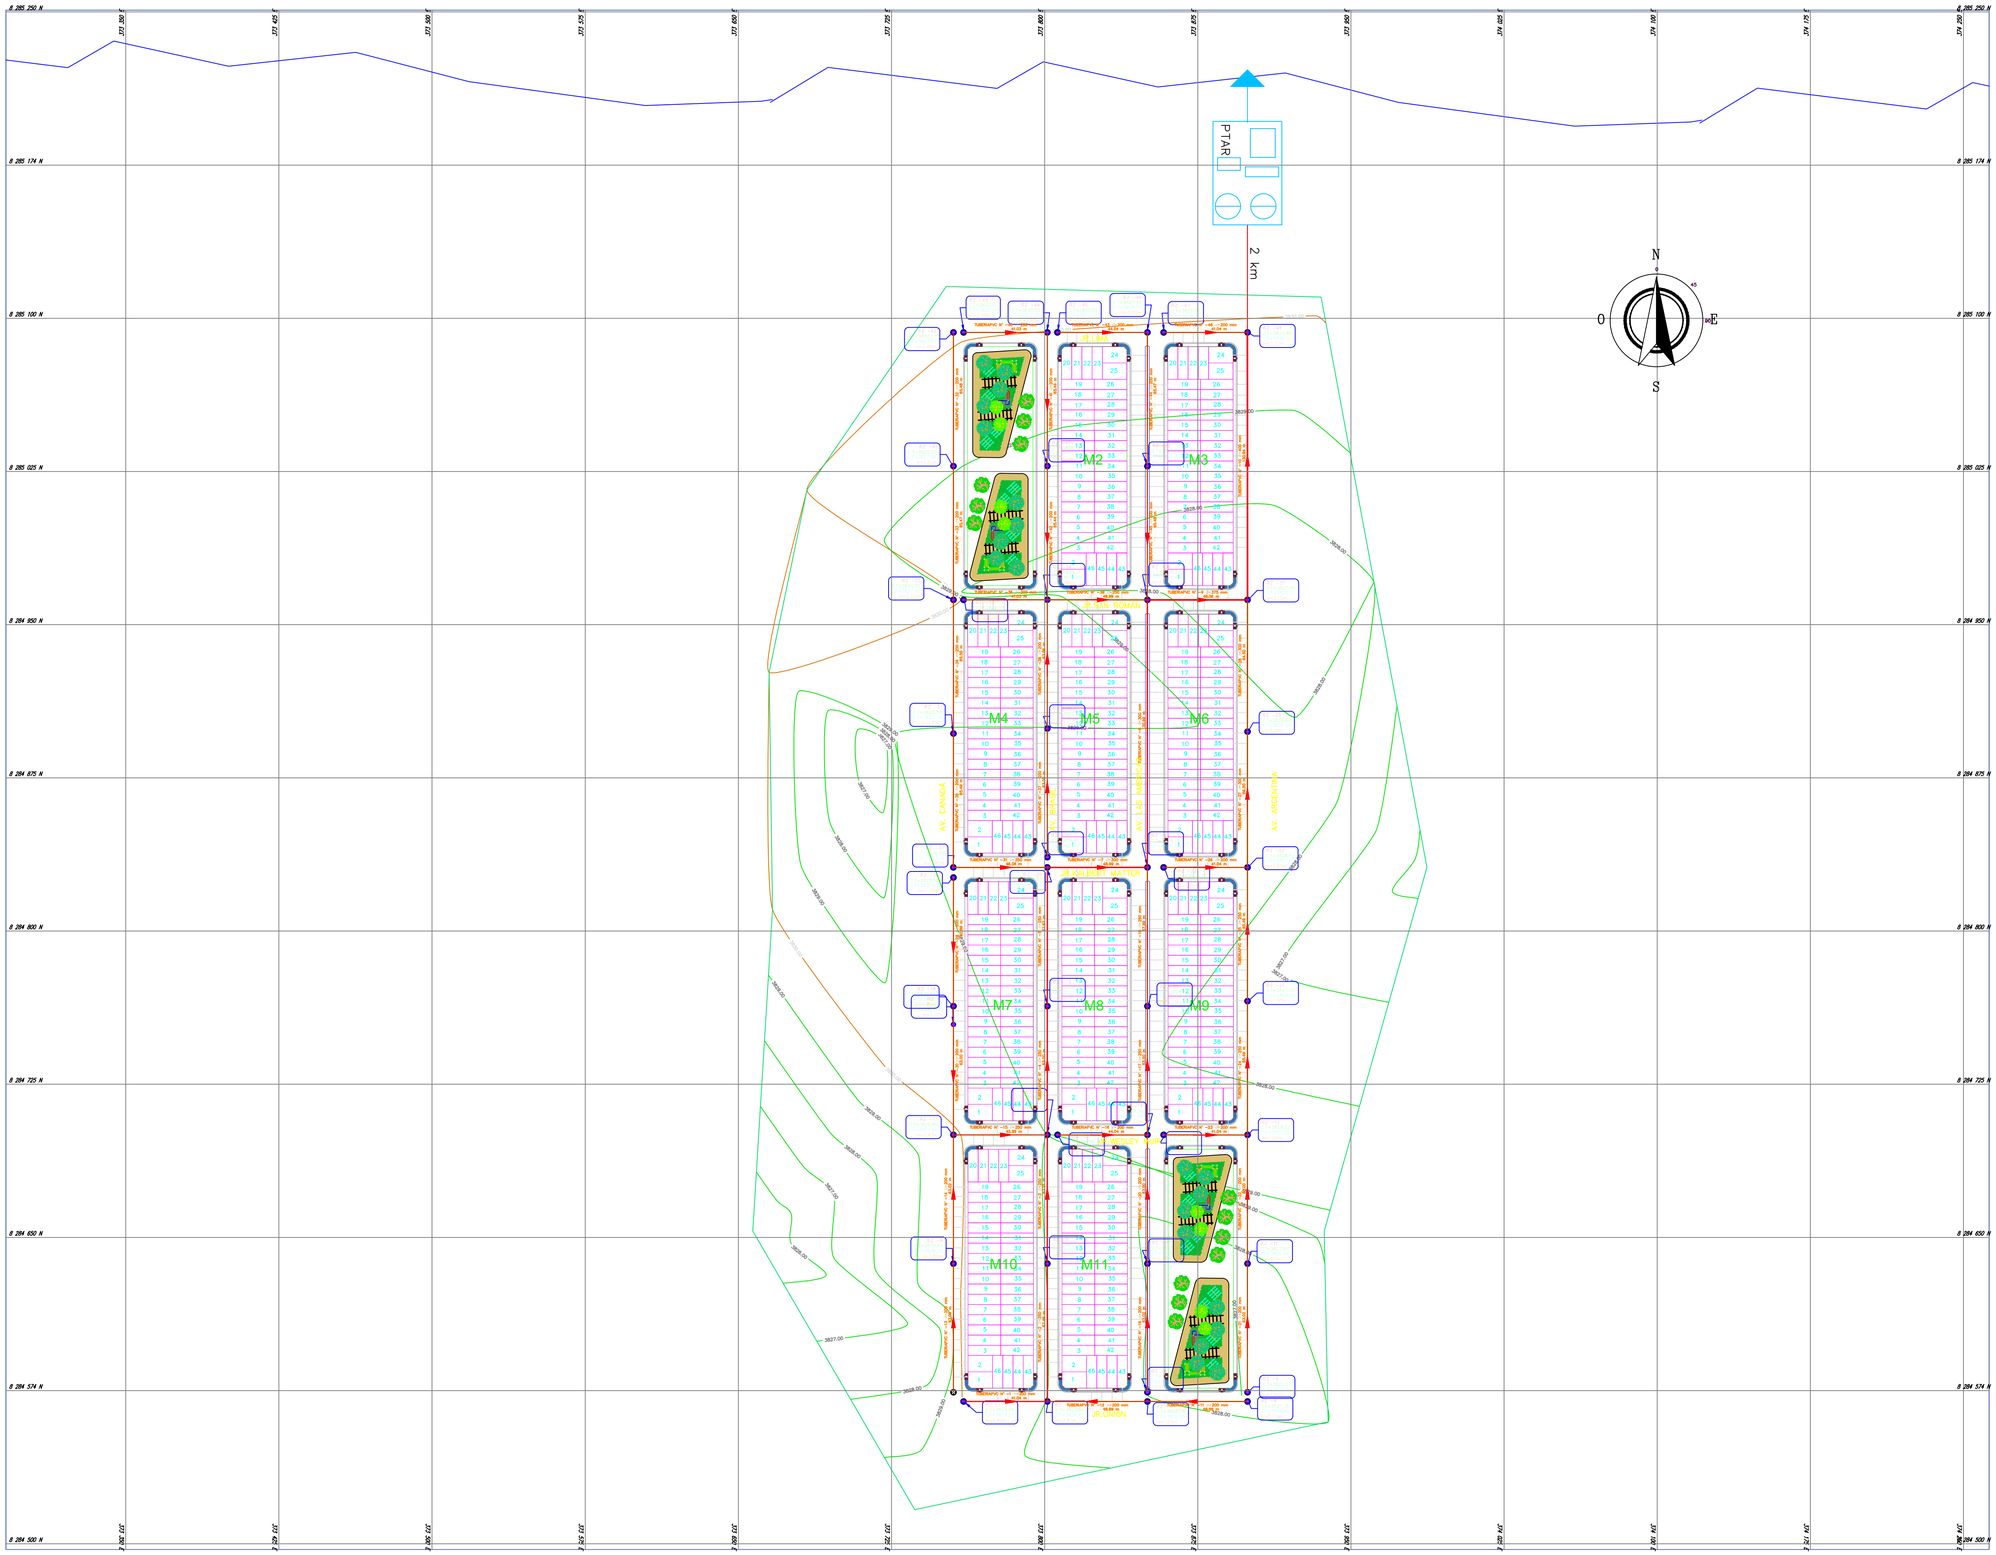

UPeU
UNIVERSIDAD PERUANA UNIÓN

NORTE

Universidad Peruana Unión
Carretera Salida a Arequipa Km. 6
Chullunquiani, Av. Héroes de la
Guerra del Pacífico, Juliaca.
COORDENADAS:
Geograficas: 15°30'48"s–70°11'03"w
Utm: 372891.5,E–8284566.5,N 3888.4,Z

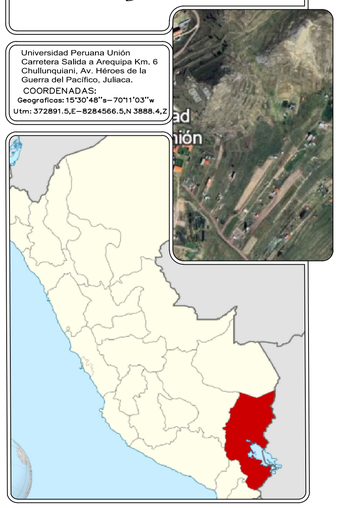

LEYENDA

Área a urbanizar	
Numeración de manzanas	M1–M2–M3
Dirección de agua residual	
Número de lotización	1–2–3–4=5
Futuros buzones para red de alcantarillado	
PTAR	PTAR
Cuerpo de agua	
Acometidas	
Red colectora principal	
Ramales colectores	

Presentado por:
- Trujillo Pajsi Alexis Romario
- Chambi Mamani Jhon Elvis
- Vilca Machaca Arnaldo
- Vargas Patiño Sebastian
- Hilasaca Barrios Kevin Samuel
- Nuñez Ochoa Kevin Anderson

Departamento: PUNO Provincia: SAN ROMAN Distrito: JULIACA	Facultad: INGENIERÍA Y ARQUITECTURA E.p: INGENIERÍA CIVIL Curso: AGUA POTABLE Y SANEAMIENTO Ciclo: VIII - G3

PROYECTO:
ABASTECIMIENTO DE AGUA POTABLE Y ALCANTARILLADO SANITARIO AL MARGEN IZQUIERDO DE LA UNIVERSIDAD PERUANA UNIÓN, SEDE JULIACA, SAN ROMÁN – PUNO

CONTIENE:
PLANO CON DISEÑO DE FUTURA RED DE ALCANTARILLADO

Escala grafica:

0 15 30 45 60 75

1: 1500

MTS

25 DE NOV 2025

09