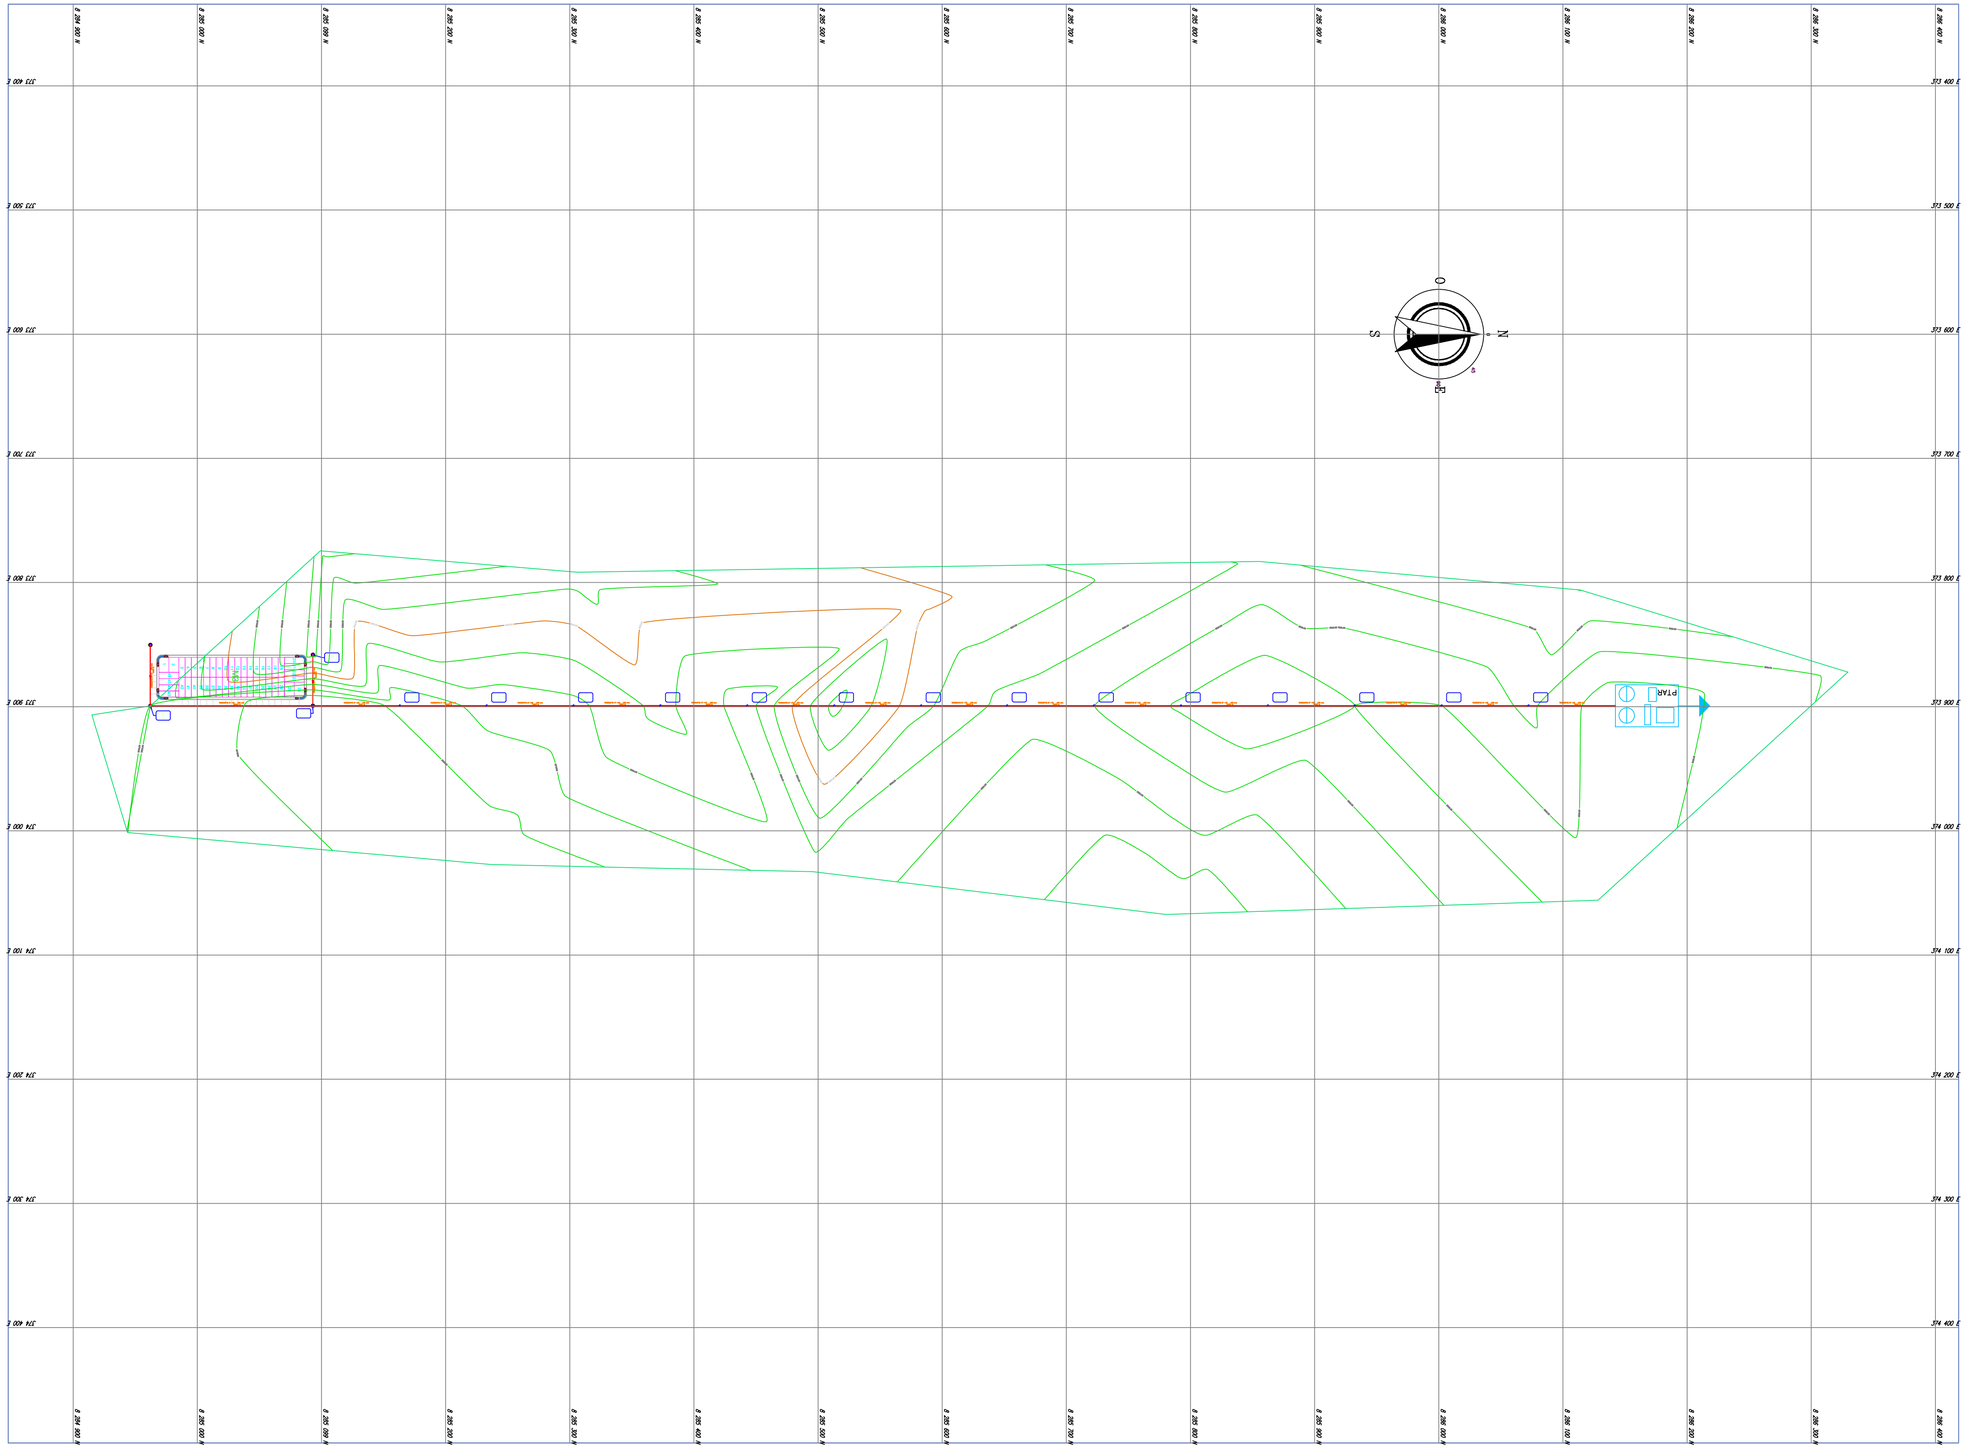

UPeU
UNIVERSIDAD PERUANA UNIÓN

NORTE

Universidad Peruana Unión
Carretera Salida a Arequipa Km. 6
Chullunquiani, Av. Héroes de la
Guerra del Pacífico, Juliaca.
COORDENADAS:
Geograficos:15°30'48"s-70°11'03"w
Utm: 372891.5,E-8284566.5,N 3888.4,Z

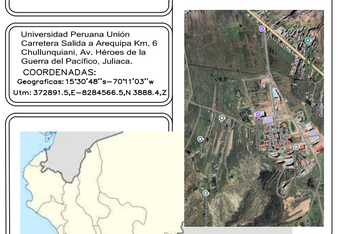

LEYENDA

- Dirección de agua residual
- Futuros buzones para red de alcantarillado
- PTAR
- Cuerpo de agua
- curvas de nivel maestras
- Red colectora principal
- Curvas de nivel secundarias

Presentado por:
- Trujillo Pajsi Alexis Romario
- Chambi Mamani Jhon Elvis
- Vilca Machaca Arnaldo
- Vargas Patiño Sebastian
- Hilasaca Barrios Kevin Samuel
- Nuñez Ochoa Kevin Anderson

Departamento: PUNO
Provincia: SAN ROMAN
Distrito: JULIACA

Facultad: INGENIERÍA Y ARQUITECTURA
E.p: INGENIERÍA CIVIL
Curso: AGUA POTABLE Y SANEAMIENTO
Ciclo: VIII - G3

PROYECTO:
ABASTECIMIENTO DE AGUA POTABLE Y ALCANTARILLADO SANITARIO AL MARGEN IZQUIERDO DE LA UNIVERSIDAD PERUANA UNIÓN, SEDE JULIACA, SAN ROMÁN – PUNO

CONTIENE:
PLANO DE LÍNEA EMISORA A PTAR

Escala grafica:
0 15 30 45 60 75

1: 1500

MTS

25 DE NOV 2025

12