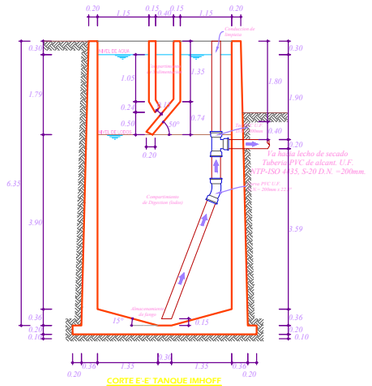

CORTE E-E TANQUE IMHOFF
Escala: 1/50

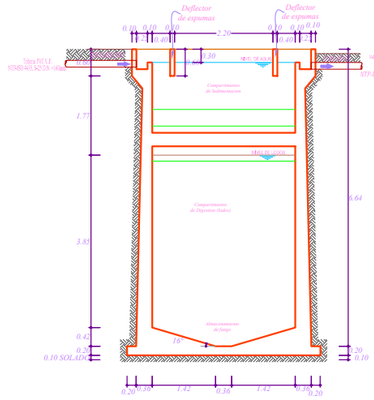

CORTE F-F TANQUE IMHOFF
Escala: 1/50

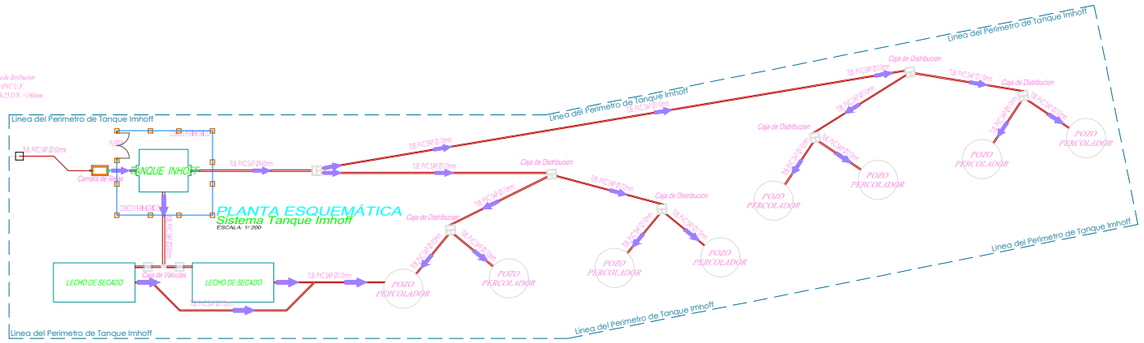

Sistema TANQUE INHOFF
ESCALA: INDICADA

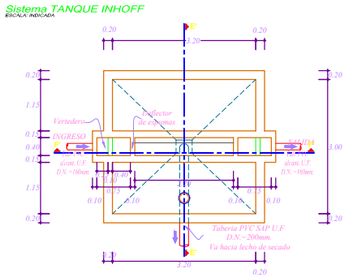

PLANTA TANQUE IMHOFF
Escala: 1/50

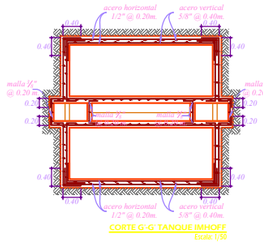

CORTE G-G TANQUE IMHOFF
Escala: 1/50

ESPECIFICACIONES TÉCNICAS

- Concreto Simple:
  - Solado: Concreto Simple SOLADO F'c=140 Kg/cm2
- Concreto Armado:
  - Concreto fc=210 Kg/cm2
- Acero Estructural Grado 60; fy = 4200 kg/cm2
  - Acero corrugado Fy=4200 kg/cm2 grado 60
- Recubrimiento:
  - Losa fondo: 3.00 cm.
  - Losa techo: 2.00 cm.
  - Muros: 3.00 cm.
- Juntas:
  - Junta vertical sin mortero.
  - Junta horizontal con mortero C:A=1:4

POZO PERCOLADOR
ESCALA: INDICADA

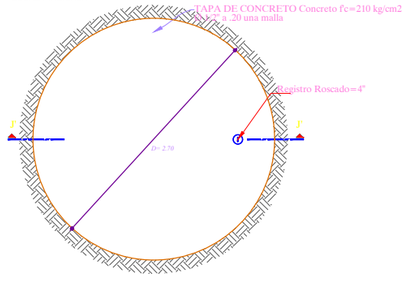

PLANTA POZO PERCOLADOR
Escala: 1/25

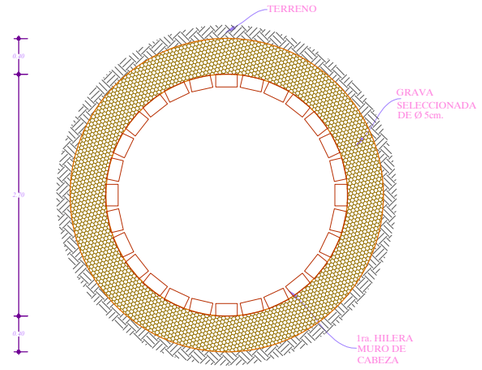

CORTE K-K' POZO PERCOLADOR
Escala: 1/25

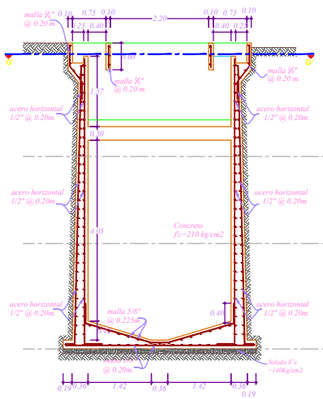

DETALLE ESTRUCTURAL TANQUE IMHOFF
Escala: 1/50

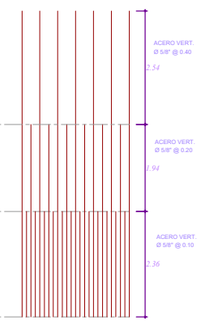

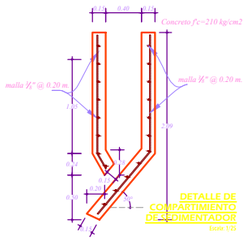

DETALLE DE COMPARTIMENTO DE SEDIMENTADOR
Escala: 1/25

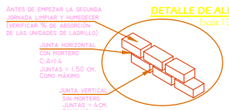

DETALLE DE ALBAÑILERIA
Escala: 1/25

DETALLE 1
Escala: 1/10

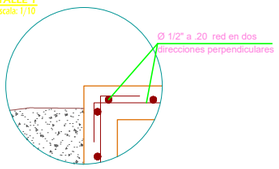

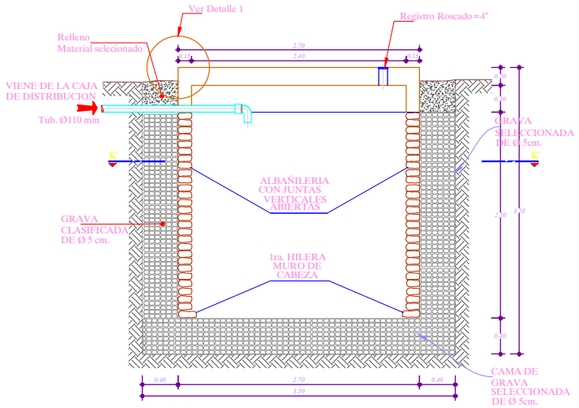

CORTE J-J' POZO PERCOLADOR
Escala: 1/25

UPeU
UNIVERSIDAD PERUANA UNIÓN

NORTE

Universidad Peruana Unión
Carretera Salida a Arequipa Km. 6
Chullunquiani, Av. Héroes de la Guerra del Pacífico, Juliaca.
COORDENADAS:
Geograficas: 15°30'48"s–70°11'03" w
Utm: 372891.5,E–8284566.5,N 3888.4,Z

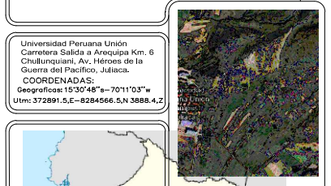

ESPECIFICACIONES TÉCNICAS

- Concreto Simple:
  - Solado: Concreto Simple SOLADO F'c=140 Kg/cm2
- Concreto Armado:
  - Concreto fc=210 Kg/cm2
- Acero Estructural Grado 60; fy = 4200 kg/cm2
  - Acero corrugado Fy=4200 kg/cm2 grado 60
- Recubrimiento:
  - Losa fondo: 3.00 cm.
  - Losa techo: 2.00 cm.
  - Muros: 3.00 cm.
- Juntas:
  - Junta vertical sin mortero.
  - Junta horizontal con mortero C:A=1:4

Presentado por:
- Trujillo Pajsi Alexis Romario
- Chambi Mamani Jhon Elvis
- Vilca Machaca Arnaldo
- Vargas Patiño Sebastian
- Hilasaca Barrios Kevin Samuel
- Nuñez Ochoa Kevin Anderson

Departamento: PUNO Provincia: SAN ROMAN Distrito: JULIACA	Facultad: INGENIERÍA Y ARQUITECTURA E.p: INGENIERÍA CIVIL Curso: AGUA POTABLE Y SANEAMIENTO Ciclo: VIII - G3

PROYECTO:
ABASTECIMIENTO DE AGUA POTABLE Y ALCANTARILLADO SANITARIO AL MARGEN IZQUIERDO DE LA UNIVERSIDAD PERUANA UNIÓN, SEDE JULIACA, SAN ROMÁN - PUNO

CONTIENE:
PLANO DE PTAR PERCOLADOR 1

Escala grafica:
0 0.75 1.5 2.25 3 3.75

1: 75

MTS

25 DE NOV 2025

26