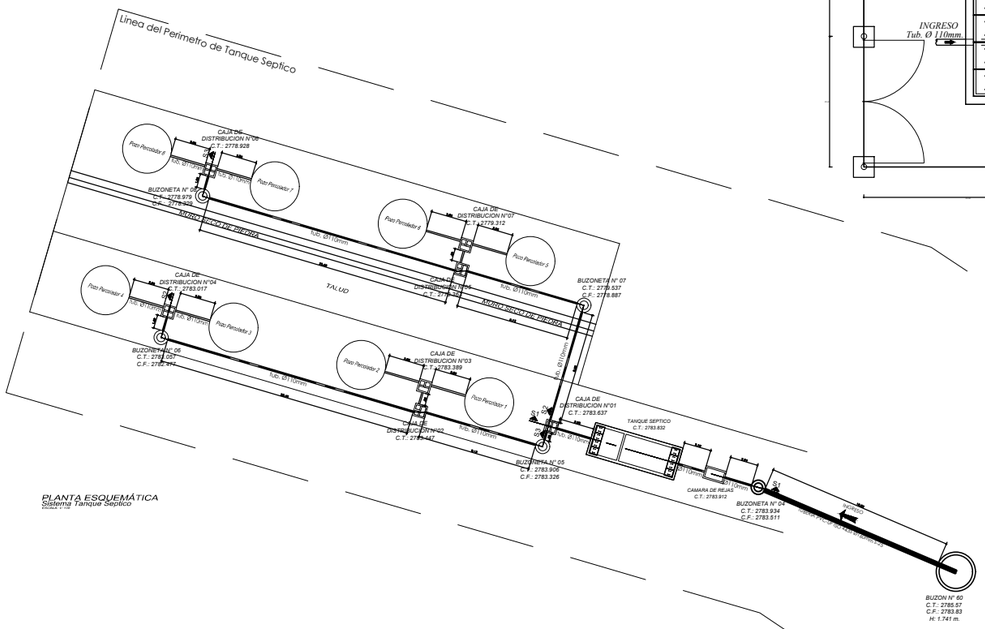

PLANTA ESQUEMÁTICA
Sistema Tanque Séptico
ESCALA 1:100

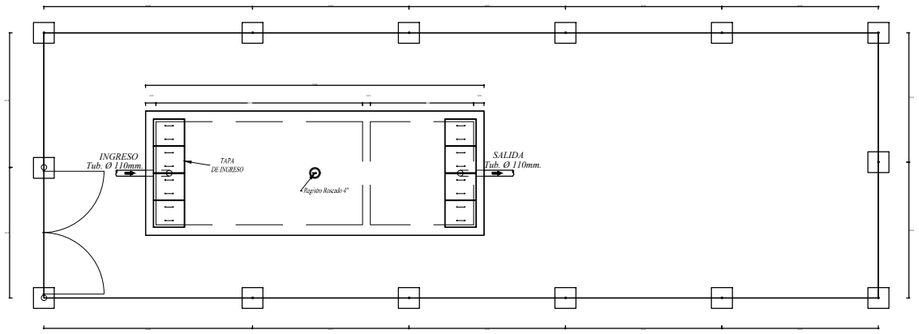

PLANTA TANQUE SEPTICO - CERCO PERMETRICO DE ALAMBRE DE PUAS
Escala: 1/50

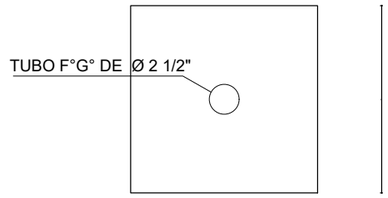

PLANTA
Escala: 1/10

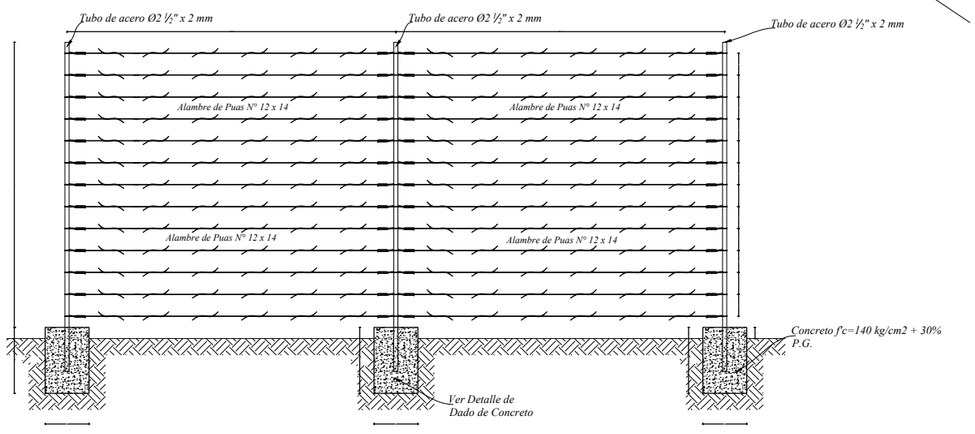

DETALLE CERCO PERIMETRICO TIPICO
Escala: 1/25

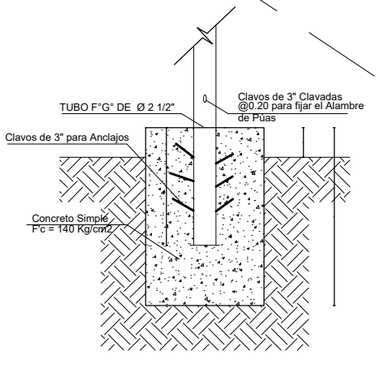

DETALLE DE DADO DE CONCRETO
Escala: 1/10

UPeU
UNIVERSIDAD PERUANA UNIÓN

NORTE

Universidad Peruana Unión
Carretera Salida a Arequipa Km. 6
Chullunquiani, Av. Héroes de la Guerra del Pacífico, Juliaca.
COORDENADAS:
Geograficas:15°30'48"s–70°11'03"w
Utm: 372891.5,E–8284566.5,N 3888.4,Z

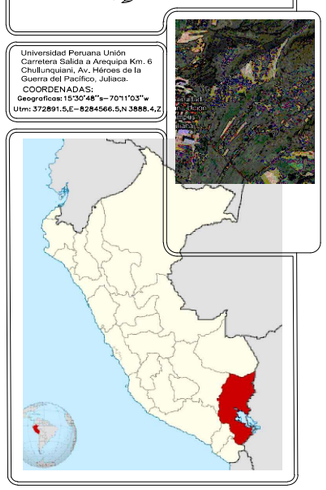

ESPECIFICACIONES TÉCNICAS

- Concreto Simple:
  Solado: Concreto Simple SOLADO F'c=140 Kg/cm2
- Concreto Armado:
  Concreto fc=210 Kg/cm2
- Acero Estructural Grado 60; fy = 4200 kg/cm2
  Acero corrugado Fy=4200 kg/cm2 grado 60
- Recubrimiento:
  Losa fondo: 3.00 cm.
  Losa techo: 2.00 cm.
  Muros: 3.00 cm.
- Juntas:
  Junta vertical sin mortero.
  Junta horizontal con mortero C:A=1:4

Presentado por:
- Trujillo Pajsi Alexis Romario
- Chambi Mamani Jhon Elvis
- Vilca Machaca Arnaldo
- Vargas Patiño Sebastian
- Hilasaca Barrios Kevin Samuel
- Nuñez Ochoa Kevin Anderson

Departamento: PUNO
Provincia: SAN ROMAN
Distrito: JULIACA

Facultad: INGENIERÍA Y ARQUITECTURA
E.p: INGENIERÍA CIVIL
Curso: AGUA POTABLE Y SANEAMIENTO
Ciclo: VIII - G3

PROYECTO:
ABASTECIMIENTO DE AGUA POTABLE Y ALCANTARILLADO SANITARIO AL MARGEN IZQUIERDO DE LA UNIVERSIDAD PERUANA UNIÓN, SEDE JULIACA, SAN ROMÁN - PUNO

CONTIENE:
PLANO DE PTAR TANQUE SÉPTICO COMPONENTES 1

Escala grafica:
0 0.75 1.5 2.25 3 3.75

1: 75

MTS

25 DE NOV 2025

27