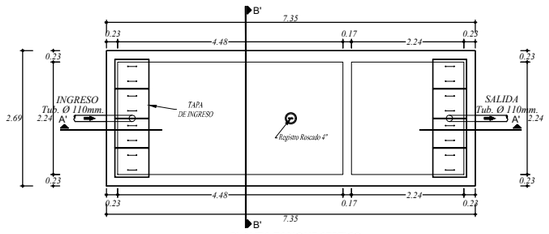

PLANTA TANQUE SEPTICO
Escala: 1/50

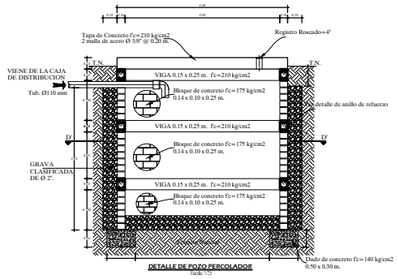

DETALLE DE POZO PERCOLADOR
Escala: 1/25

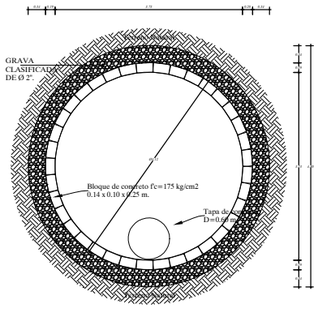

CORTE D'-D' POZO PERCOLADOR
Escala: 1/25

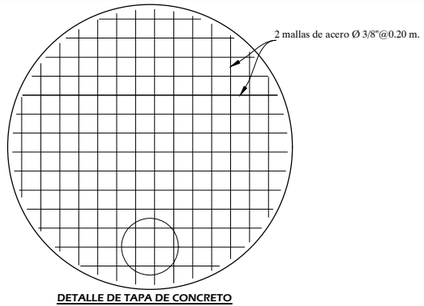

DETALLE DE TAPA DE CONCRETO
Escala: 1/25

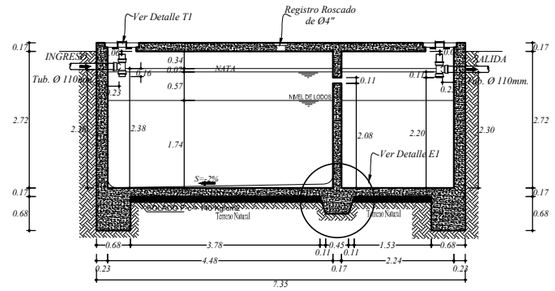

CORTE A-A TANQUE SEPTICO
Escala: 1/50

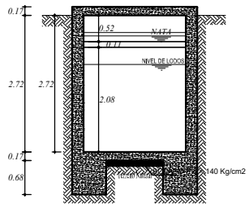

CORTE B'-B' TANQUE SEPTICO
Escala: 1/50

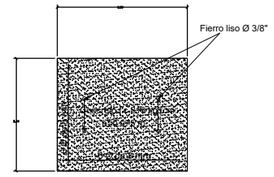

DETALLE T1
Escala: 1/20

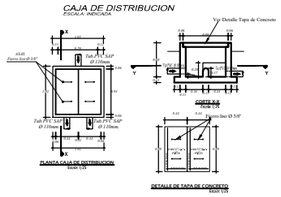

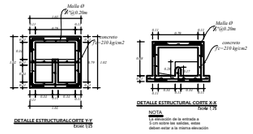

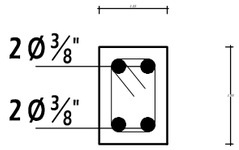

Estribos Ø¼" : @0.20 m.

Anillo de refuerzo

Escala: 1/25

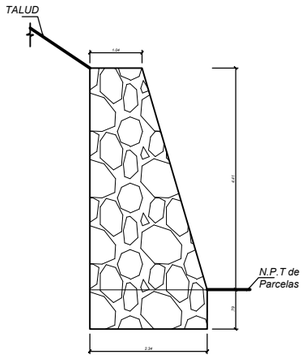

Detalle de Muro Seco Tipico
ESC: 1/25

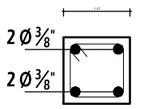

Estribos Ø¼" : 1@0.05, 4@0.10
Rto. 0.15m.

C-1

Escala: 1/25

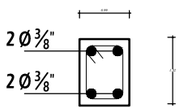

Estribos Ø¼" : 1@0.05, 4@0.10
Rto. 0.15m.

C-2

Escala: 1/25

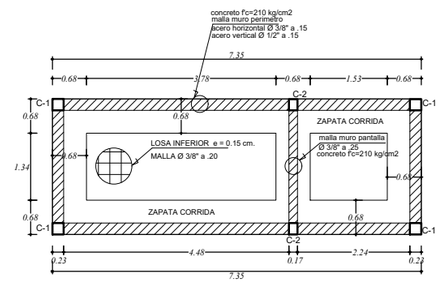

CIMENTACION TANQUE SEPTICO
Escala: 1/50

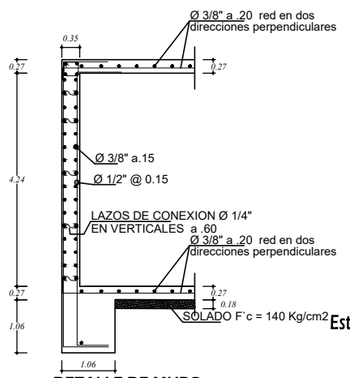

DETALLE DE MURO
Escala: 1/50

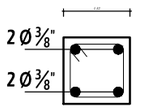

Estribos Ø¼" : 1@0.05, 4@0.10
Rto. 0.15m.

V-1

Escala: 1/25

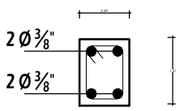

Estribos Ø¼" : 1@0.05, 4@0.10
Rto. 0.15m.

V-2

Escala: 1/25

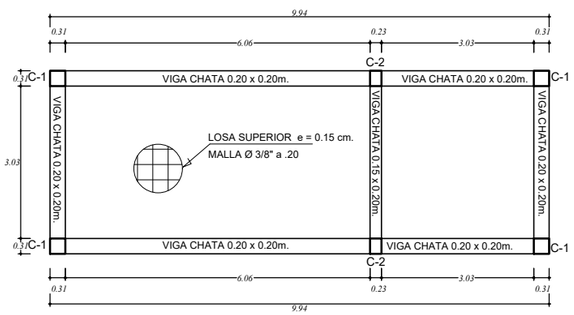

LOSA MACIZA TANQUE SEPTICO
Escala: 1/50

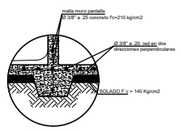

DETALLE E1
Escala 1/25

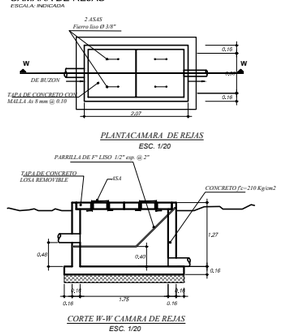

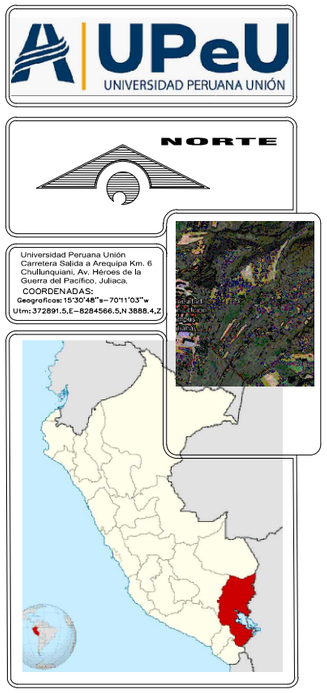

ESPECIFICACIONES TÉCNICAS

- Concreto Simple:
  - Solado: Concreto Simple SOLADO F´c=140 Kg/cm2
- Concreto Armado:
  - Concreto f'c=210 Kg/cm2
- Acero Estructural Grado 60; fy = 4200 kg/cm2
  - Acero corrugado f'y=4200 kg/cm2 grado 60
- Recubnmiento:
  - Losa fondo: 3.00 cm.
  - Losa techo: 2.00 cm.
  - Muros: 3.00 cm.
- Juntas:
  - Junta vertical sin mortero.
  - Junta horizontal con mortero C:A= 1:4

Presentado por:
- Trujillo Pajsi Alexis Romario
- Chambi Mamani Jhon Elvis
- Vilca Machaca Arnaldo
- Vargas Patiño Sebastian
- Hilasaca Barrios Kevin Samuel
- Nuñez Ochoa Kevin Anderson

Departamento: PUNO
Provincia: SAN ROMAN
Distrito: JULIACA

Facultad: INGENIERÍA Y ARQUITECTURA
E.p: INGENIERÍA CIVIL
Curso: AGUA POTABLE Y SANEAMIENTO
Ciclo: VIII - G3

PROYECTO:
ABASTECIMIENTO DE AGUA POTABLE Y ALCANTARILLADO SANITARIO AL MARGEN IZQUIERDO DE LA UNIVERSIDAD PERUANA UNIÓN, SEDE JULIACA, SAN ROMÁN - PUNO

CONTIENE:
PLANO DE PTAR TANQUE SÉPTICO COMPONENTES 2

Escala grafica:
0 0.75 1.5 2.25 3 3.75

1: 75

MTS

25 DE NOV 2025

28