CARACTERISTICAS DE CANTERAS
RESUMEN DE UBICACIÓN DE MATERIALES DE CONSTRUCCION (CANTERAS)
CONTROL DE CALIDAD EN LA CONFORMACION DE TERRAPLEN DEL CANAL DE RIEGO CANAL "N"

Nº	Nombre de Cantera	Ubicación (Km)	Acceso		Lado	Area (m2)	Espesor (m)	Volumen (m3)	Rend. %	Utilidad	Tratamiento	Origen del Mterial
			Estado	Longitud (Km)								
1.00 MATERIAL DE AGREGADO												
1	**MATERIAL AGREGADO MA-01 (HORMIGON) RIO LLALLIMAYO**	2+000 - 5+000	MAL	0.8 DESDE EL C.L - 02 Y A 1.00 DE BOCATOMA	Der.	150,000.00	1.5	225,000.00	85%	TERRAPLEN CONGRETO HIDRAULICO	ACUMULACION ZARANDEO	ALUVIAL
2.00 CANTERAS DE MATERIAL LIGANTE												
1	**MATERIAL DE LIGANTE ML-01 (LIGANTE)**	3+970	MAL NO EXISTE	0.10 DESDE EL C.P.	Izq.	2,500.00	2	5,000.00	80%	TERRAPEN	ACUMULACION ZARANDEO	COLUVIAL
3.00 CANTERAS DE MATERIAL RELLENO												
1	**MATERIAL DE RELLENO MR-01**	4+500	MAL	0.50 DESDE EL C.P.	Izq.	10,000.00	2	20,000.00	85%	TERRAPEN	ACUMULACION ZARANDEO	COLUVIAL
2	**MATERIAL DE RELLENO MR-02 (AQUESAYA)**	8+600	MAL	0.30 DESDE EL C.P.	Izq.	20,000.00	4	80,000.00	75%	TERRAPEN	ACUMULACION ZARANDEO	ALUVIAL
3	**MATERIAL DE RELLENO MR-03 (FINAYA)**	3+300	MAL NO EXISTE	0.30 DESDE EL C.L 05	Izq.	10,000.00	4	40,000.00	75%	TERRAPEN	ACUMULACION ZARANDEO	COLUVIAL Y RESIDUAL
4	**MATERIAL DE RELLENO MR-04 (SANTA LUCIA)**	1+000	REGULAR A BUENO	0.20 DESDE EL C.L. 03	Der.	60,000.00	3	180,000.00	80%	TERRAPEN	ACUMULACION ZARANDEO	COLUVIAL Y RESIDUAL
4.00 CANTERAS DE ROCA												
1	**CANTERA DE ROCA CR-01**	8+425	MAL	1.10 DESDE EL C.P.	Izq.	40,000.00	5	200,000.00	85%	GAVIONES ENROCADO OBRAS DE ARTE	VOLADURA	ROCAS SEDIMENTARIA
5.00 FUENTE DE AGUA												
1	**FUENTE DE AGUA FA - 01 RIO LLALLIMAYO**	PARALELO AL TRAMO C.L 02 MARGEN	REGULAR	**PROMEDIO** 800.00	Der.	PERMANENTE			100%	CONGRETO HIDRAULICO TERRAPLEN	BOMBEO	RIO LLALLIMAYO

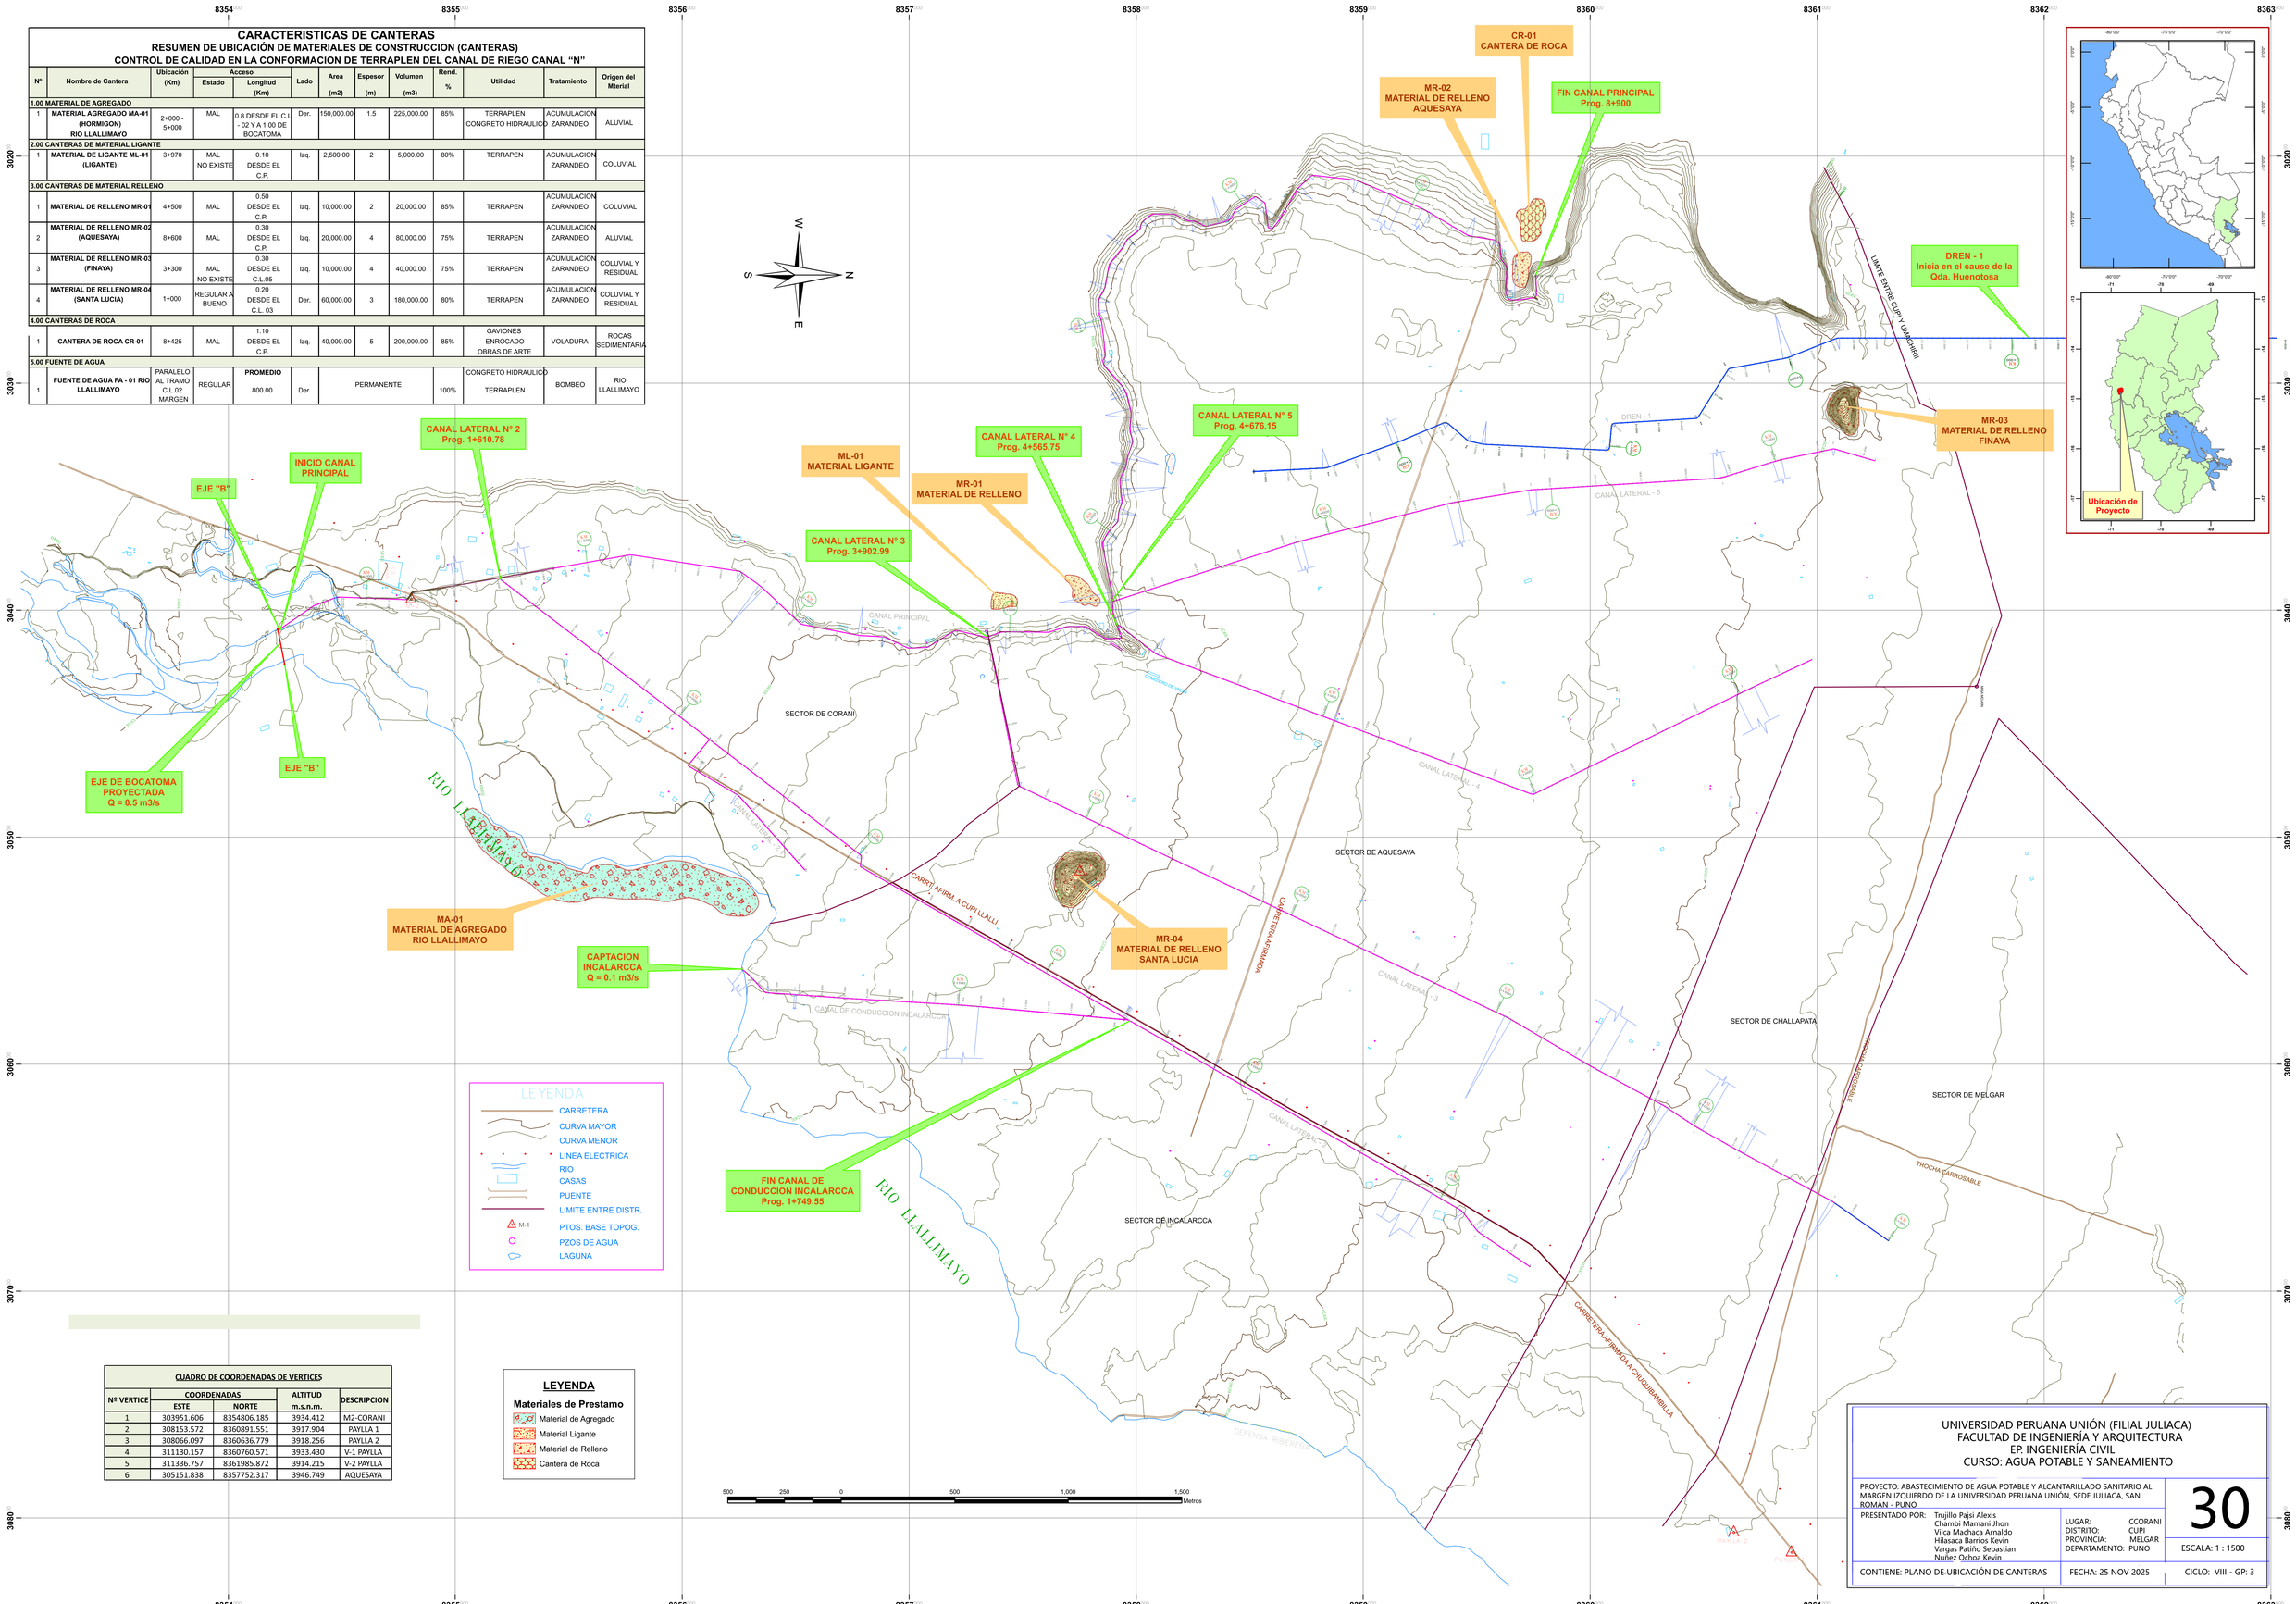

CUADRO DE COORDENADAS DE VERTICES				
Nº VERTICE	COORDENADAS		ALTITUD m.s.n.m.	DESCRIPCION
	ESTE	NORTE		
1	303951.606	8354806.185	3934.412	M2-CORANI
2	308153.572	8360891.551	3917.904	PAYLLA 1
3	308066.097	8360636.779	3918.256	PAYLLA 2
4	311130.157	8360760.571	3933.430	V-1 PAYLLA
5	311336.757	8361985.872	3914.215	V-2 PAYLLA
6	305151.838	8357752.317	3946.749	AQUESAYA

LEYENDA

Materiales de Prestamo

- Material de Agregado
- Material Ligante
- Material de Relleno
- Cantera de Roca

UNIVERSIDAD PERUANA UNIÓN (FILIAL JULIACA)
FACULTAD DE INGENIERÍA Y ARQUITECTURA
EP. INGENIERÍA CIVIL
CURSO: AGUA POTABLE Y SANEAMIENTO

PROYECTO: ABASTECIMIENTO DE AGUA POTABLE Y ALCANTARILLADO SANITARIO AL MARGEN IZQUIERDO DE LA UNIVERSIDAD PERUANA UNIÓN, SEDE JULIACA, SAN ROMÁN - PUNO

PRESENTADO POR: Trujillo Pajsi Alexis
Chambi Mamani Jhon
Vilca Machaca Arnaldo
Hilasaca Barrios Kevin
Vargas Patiño Sebastian
Nuñez Ochoa Kevin

LUGAR: CCORANI
DISTRITO: CUPI
PROVINCIA: MELGAR
DEPARTAMENTO: PUNO

30

ESCALA: 1 : 1500

CONTIENE: PLANO DE UBICACIÓN DE CANTERAS

FECHA: 25 NOV 2025

CICLO: VIII - GP: 3